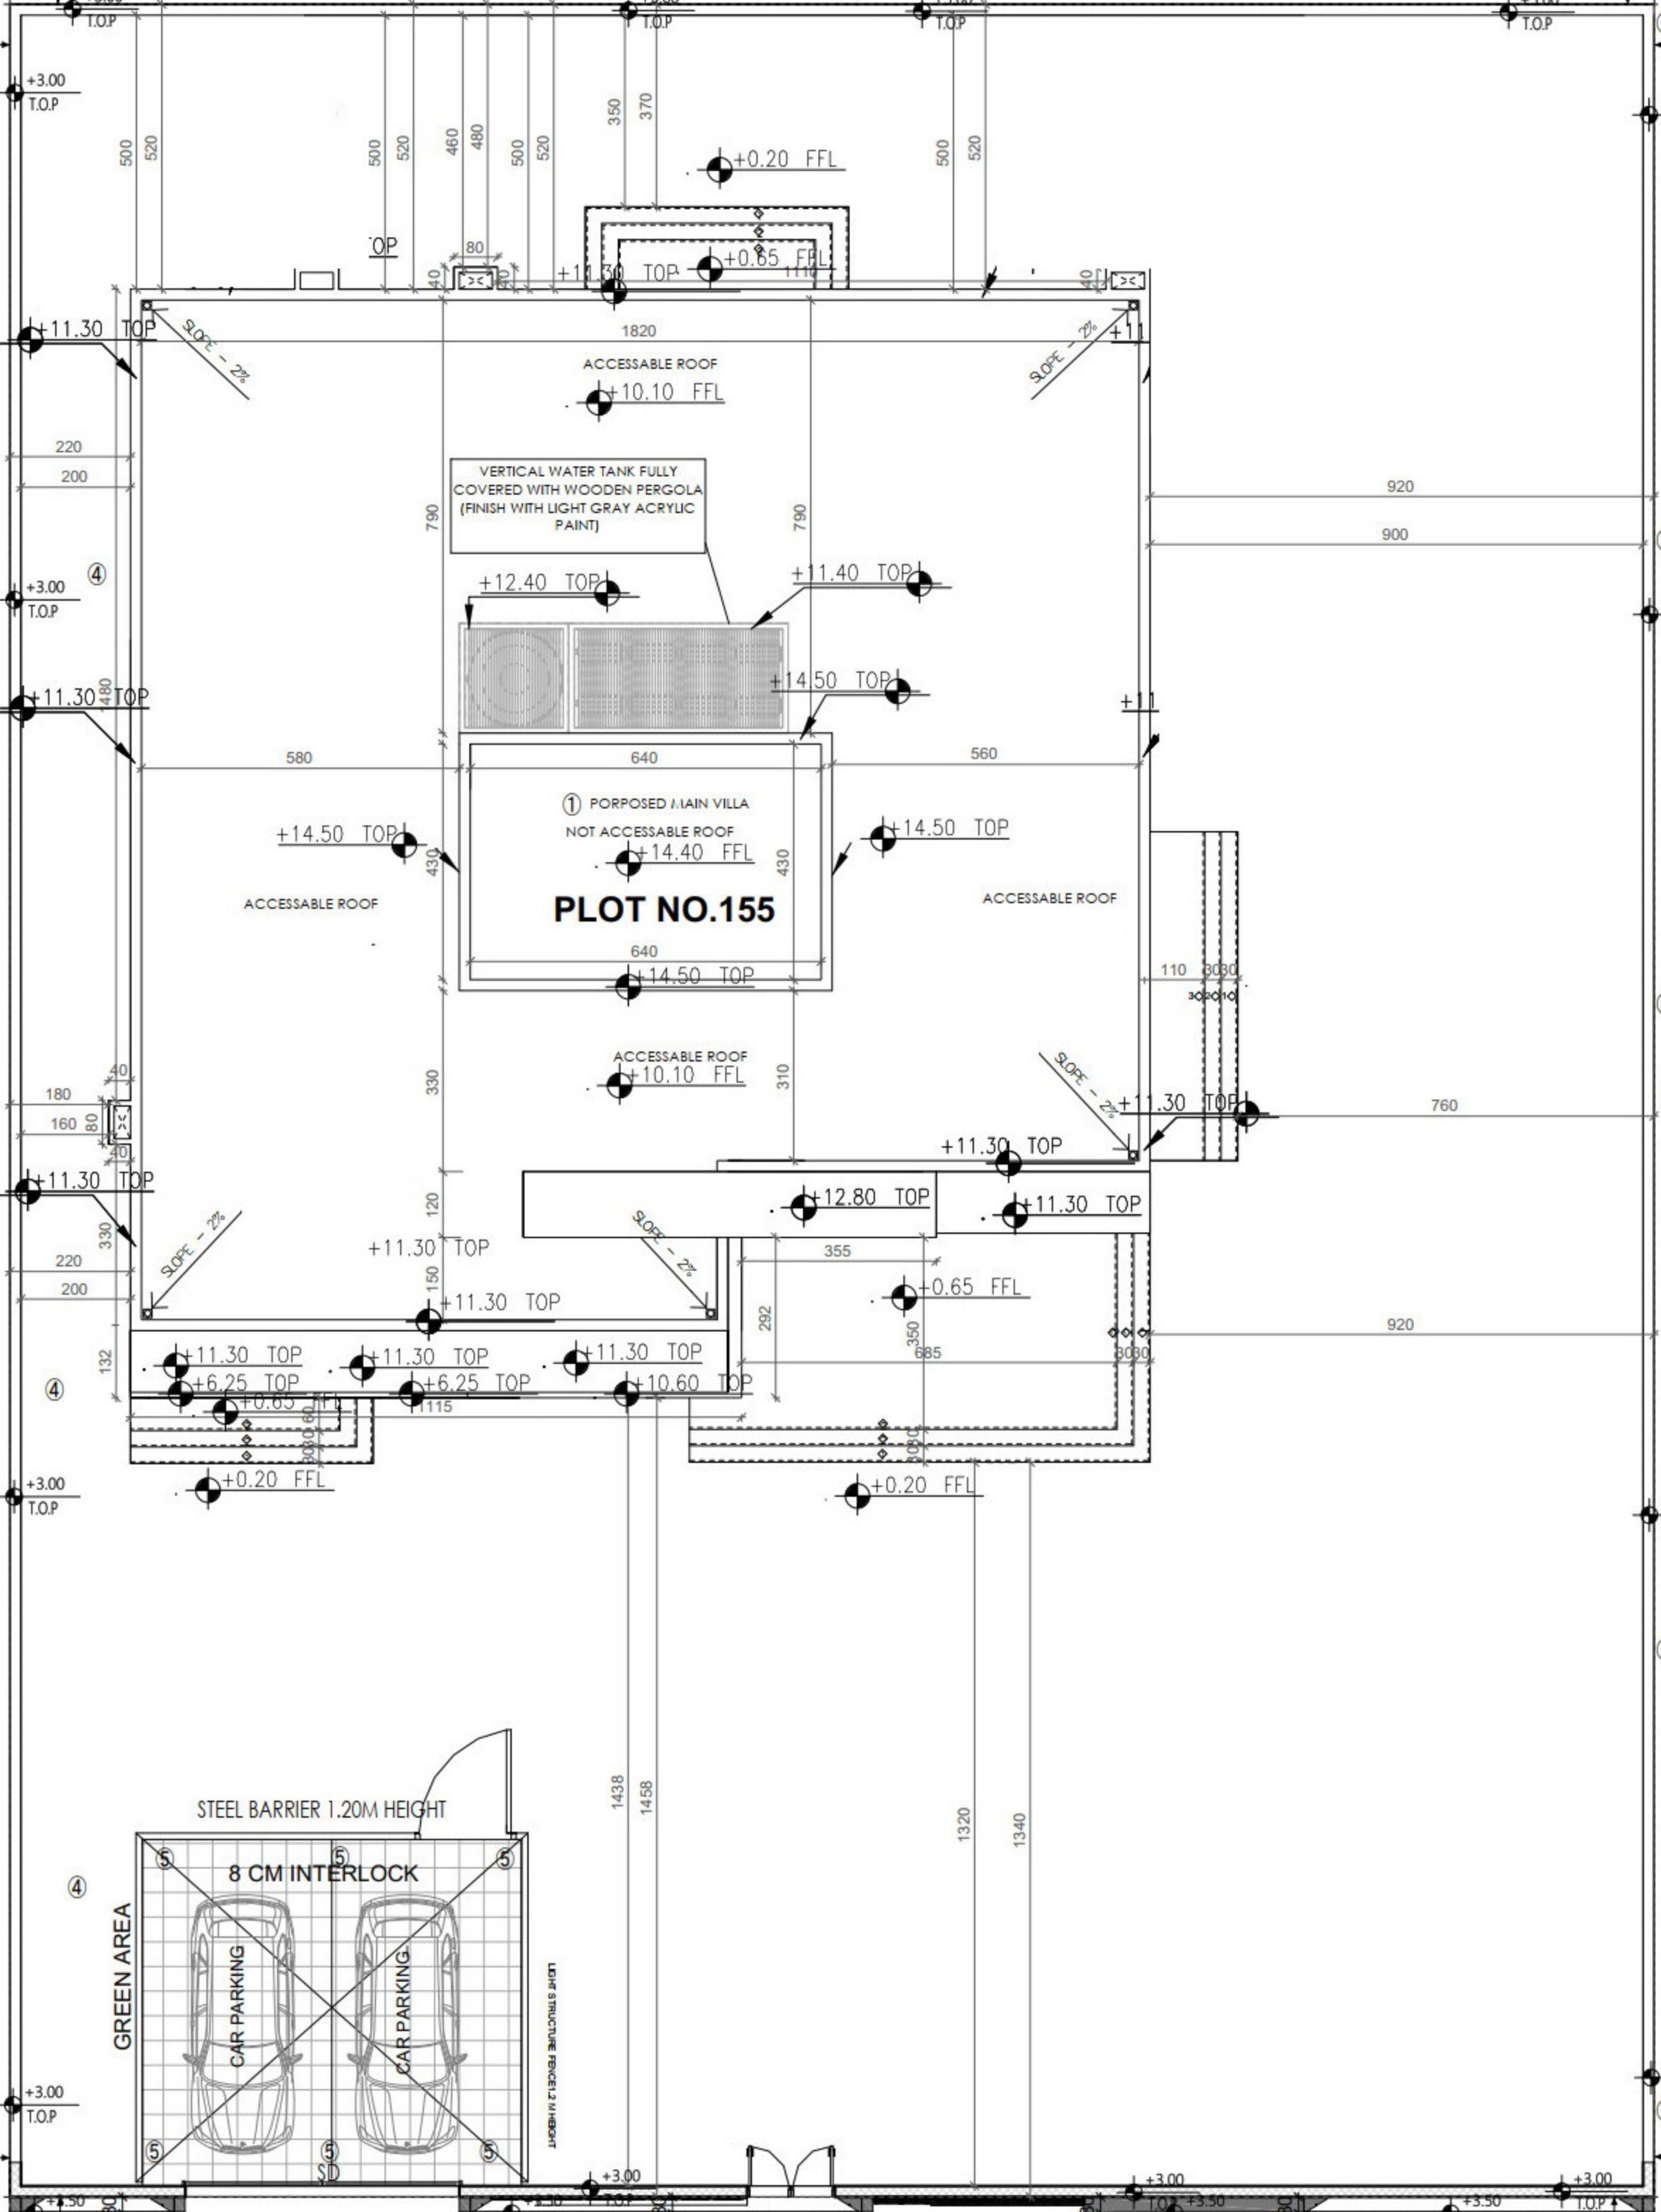
+3.00
T.O.P
+0.20 FFL
+0.65 FFL
+11.30 TOP
ACCESSABLE ROOF
+10.10 FFL
VERTICAL WATER TANK FULLY COVERED WITH WOODEN PERGOLA (FINISH WITH LIGHT GRAY ACRYLIC PAINT)
+12.40 TOP
+11.40 TOP
+14.50 TOP
① PORPOSED MAIN VILLA
NOT ACCESSABLE ROOF
+14.40 FFL
PLOT NO.155
SLOPE - 2%
+12.80 TOP
+6.25 TOP
+10.60 TOP
STEEL BARRIER 1.20M HEIGHT
8 CM INTERLOCK
GREEN AREA
CAR PARKING
LIGHT STRUCTURE FENCE1.2 M HEIGHT
SD

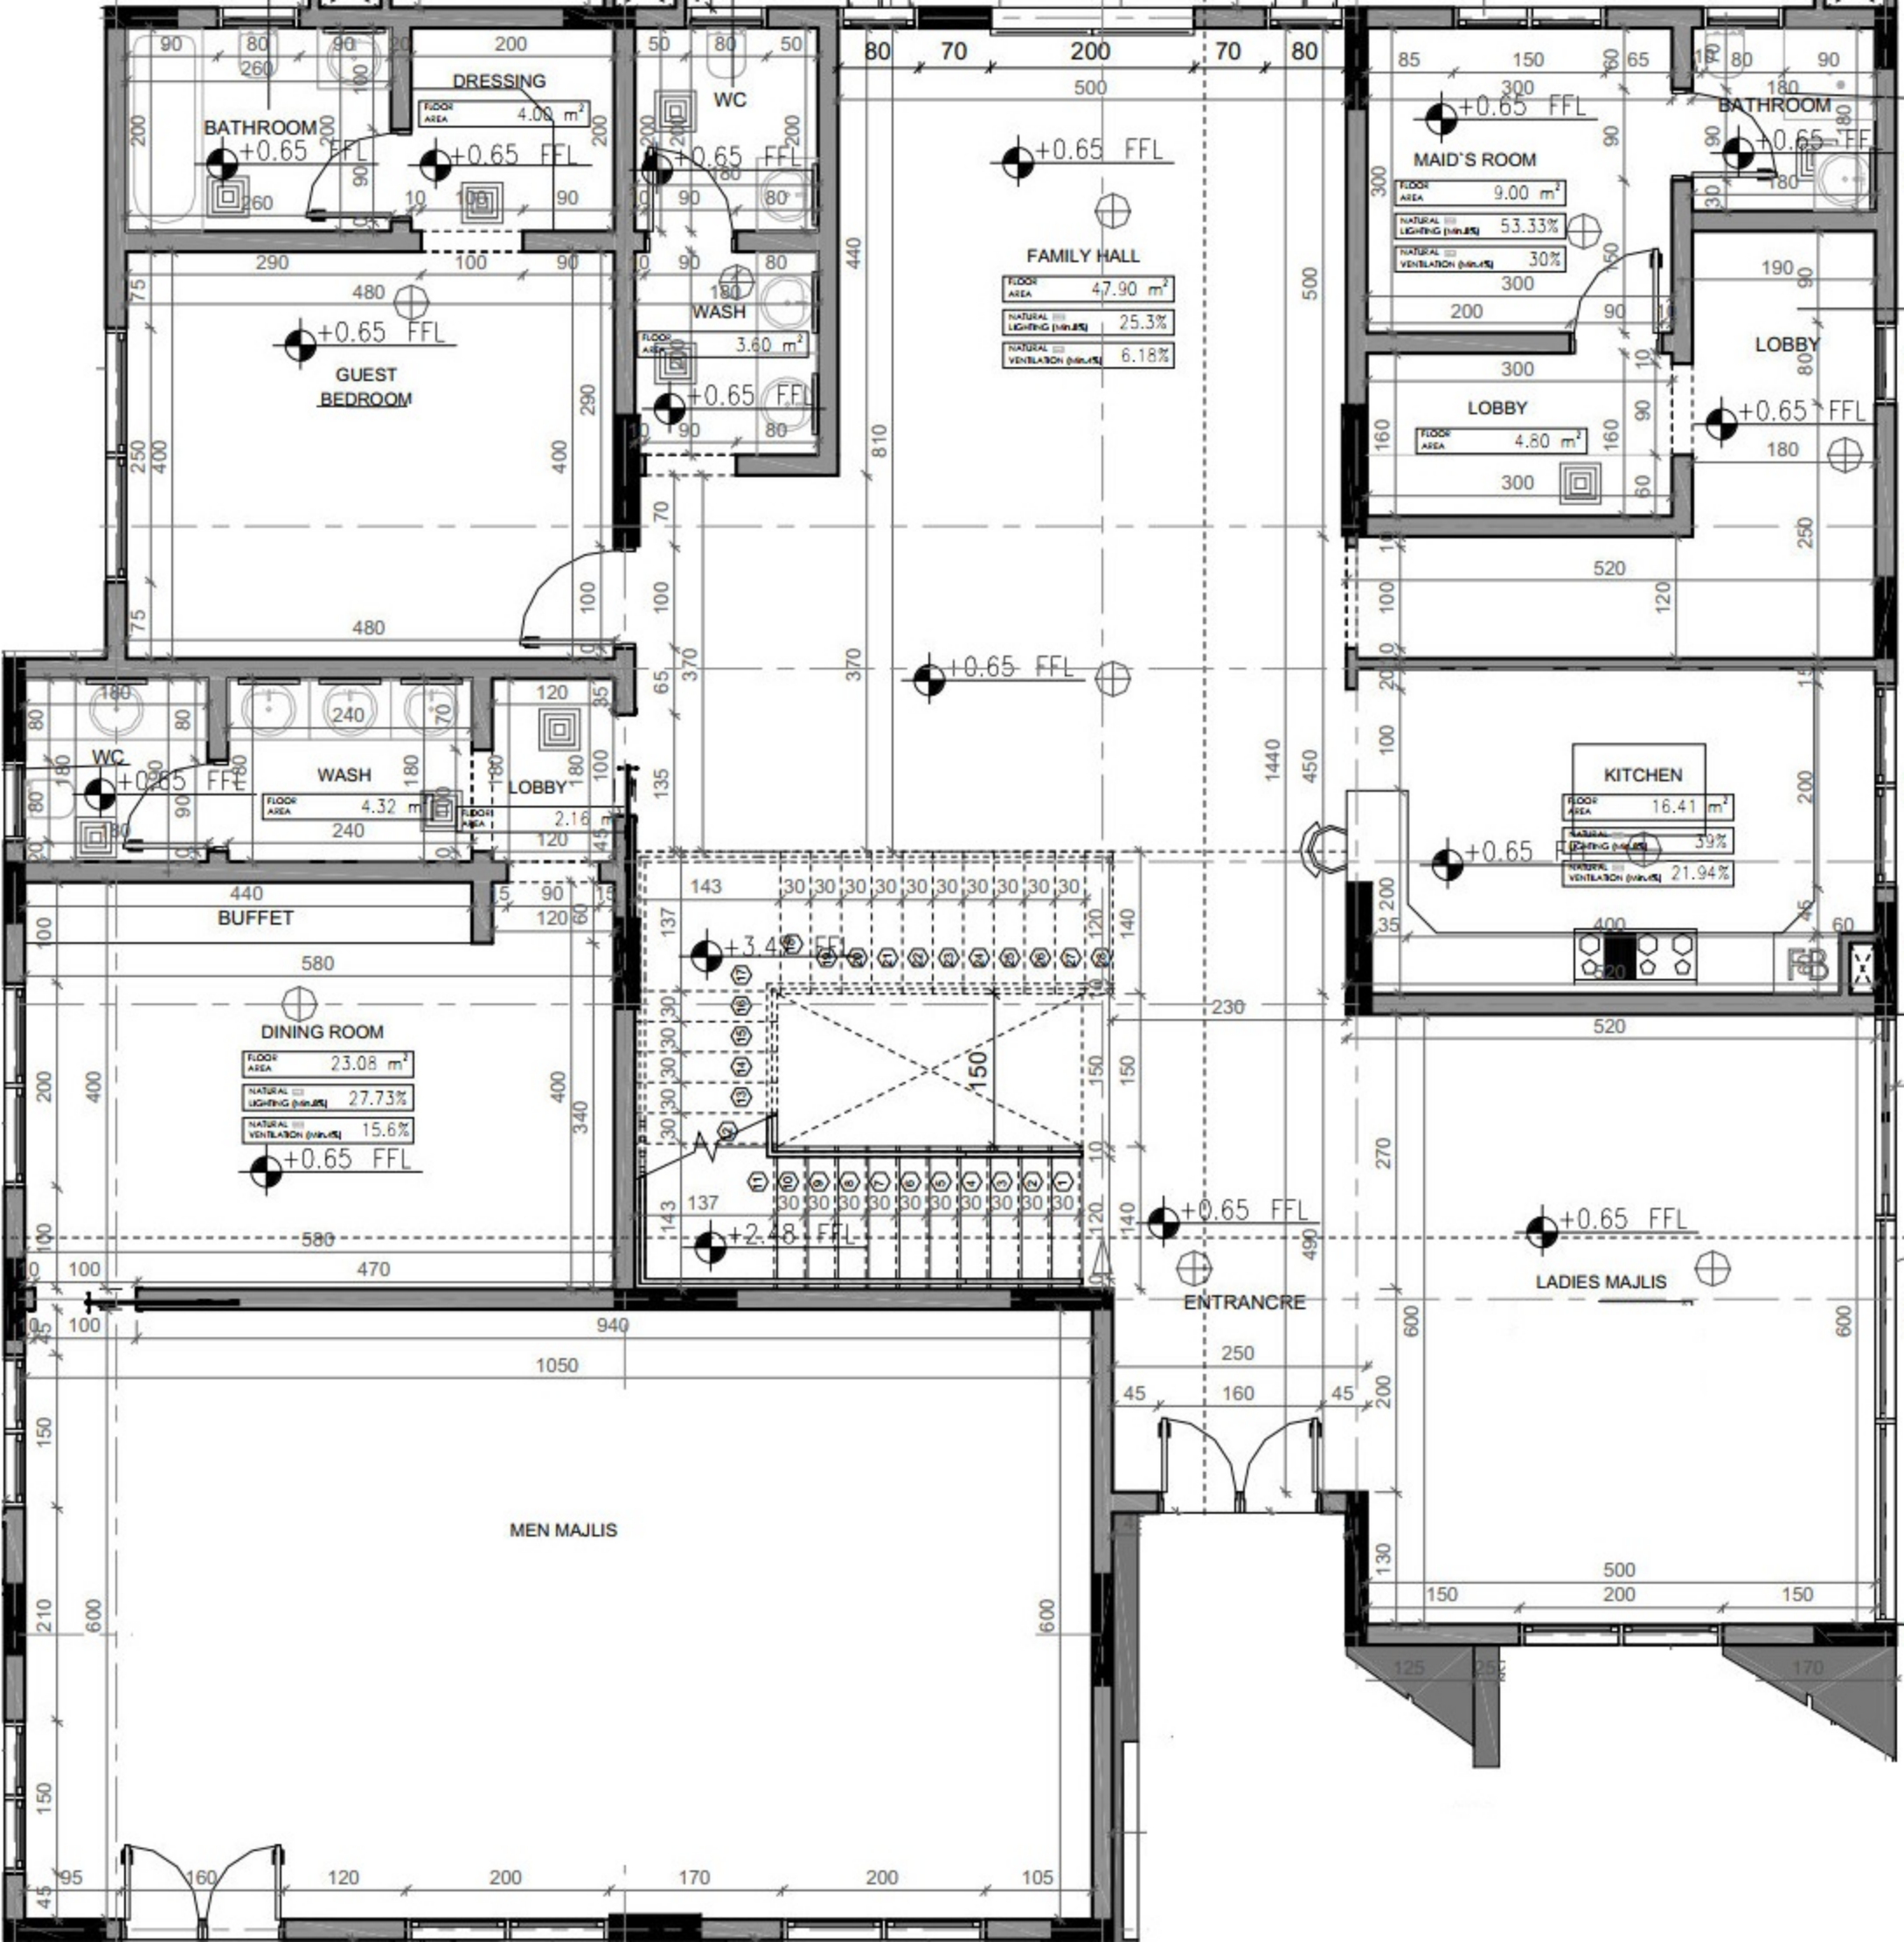
BATHROOM
+0.65 FFL
DRESSING
FLOOR AREA 4.00 m²
WC
+0.65 FFL
FAMILY HALL
FLOOR AREA 47.90 m²
NATURAL LIGHTING (MIN.8%) 25.3%
NATURAL VENTILATION (MIN.4%) 6.18%
MAID`S ROOM
FLOOR AREA 9.00 m²
NATURAL LIGHTING (MIN.8%) 53.33%
NATURAL VENTILATION (MIN.4%) 30%
BATHROOM
GUEST BEDROOM
WASH
FLOOR AREA 3.60 m²
LOBBY
FLOOR AREA 4.80 m²
LOBBY
WC
WASH
FLOOR AREA 4.32 m²
LOBBY
FLOOR AREA 2.16 m²
KITCHEN
FLOOR AREA 16.41 m²
NATURAL LIGHTING (MIN.8%) 39%
NATURAL VENTILATION (MIN.4%) 21.94%
BUFFET
DINING ROOM
FLOOR AREA 23.08 m²
NATURAL LIGHTING (MIN.8%) 27.73%
NATURAL VENTILATION (MIN.4%) 15.6%
+3.48 FFL
+2.48 FFL
ENTRANCRE
LADIES MAJLIS
MEN MAJLIS

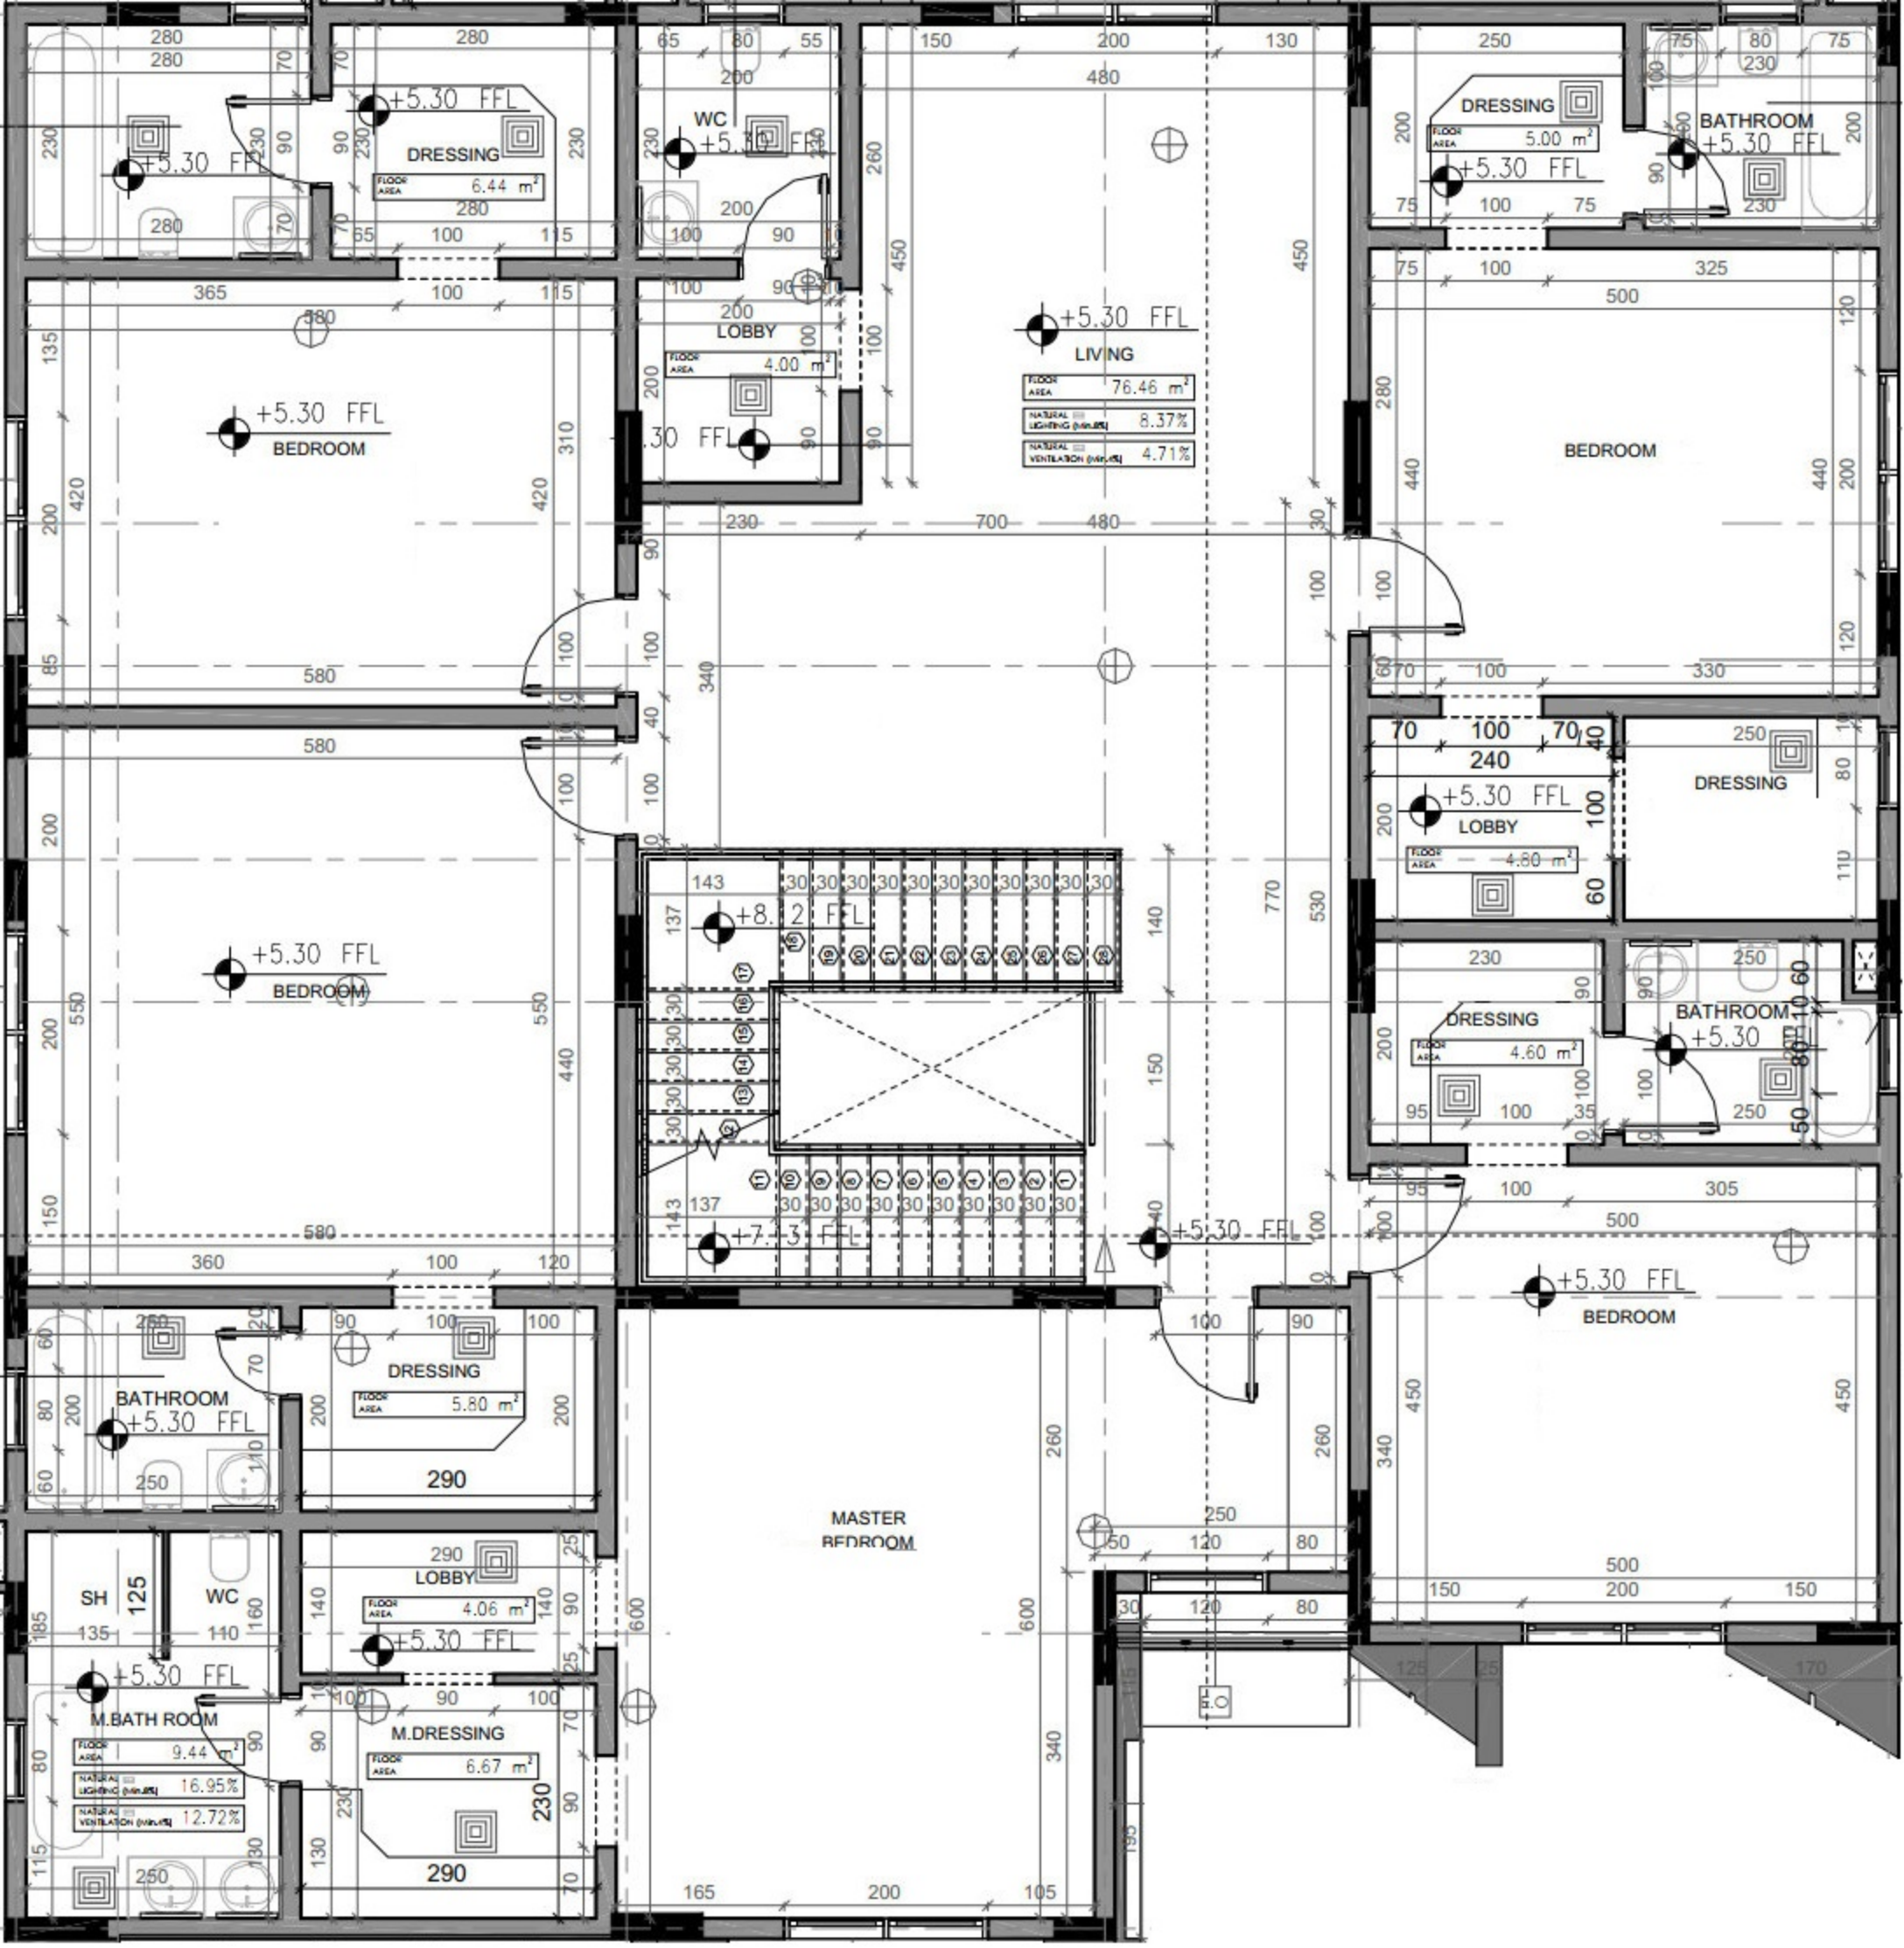
DRESSING
FLOOR AREA 6.44 m²
+5.30 FFL
WC
LOBBY
FLOOR AREA 4.00 m²
LIVING
FLOOR AREA 76.46 m²
NATURAL LIGHTING (MIN.8%) 8.37%
NATURAL VENTILATION (MIN.4%) 4.71%
BEDROOM
DRESSING
FLOOR AREA 5.00 m²
BATHROOM
LOBBY
FLOOR AREA 4.80 m²
DRESSING
FLOOR AREA 4.60 m²
BATHROOM
+8.12 FFL
+7.73 FFL
BATHROOM
DRESSING
FLOOR AREA 5.80 m²
MASTER BEDROOM
SH
WC
LOBBY
FLOOR AREA 4.06 m²
M.BATH ROOM
FLOOR AREA 9.44 m²
NATURAL LIGHTING (MIN.8%) 16.95%
NATURAL VENTILATION (MIN.4%) 12.72%
M.DRESSING
FLOOR AREA 6.67 m²

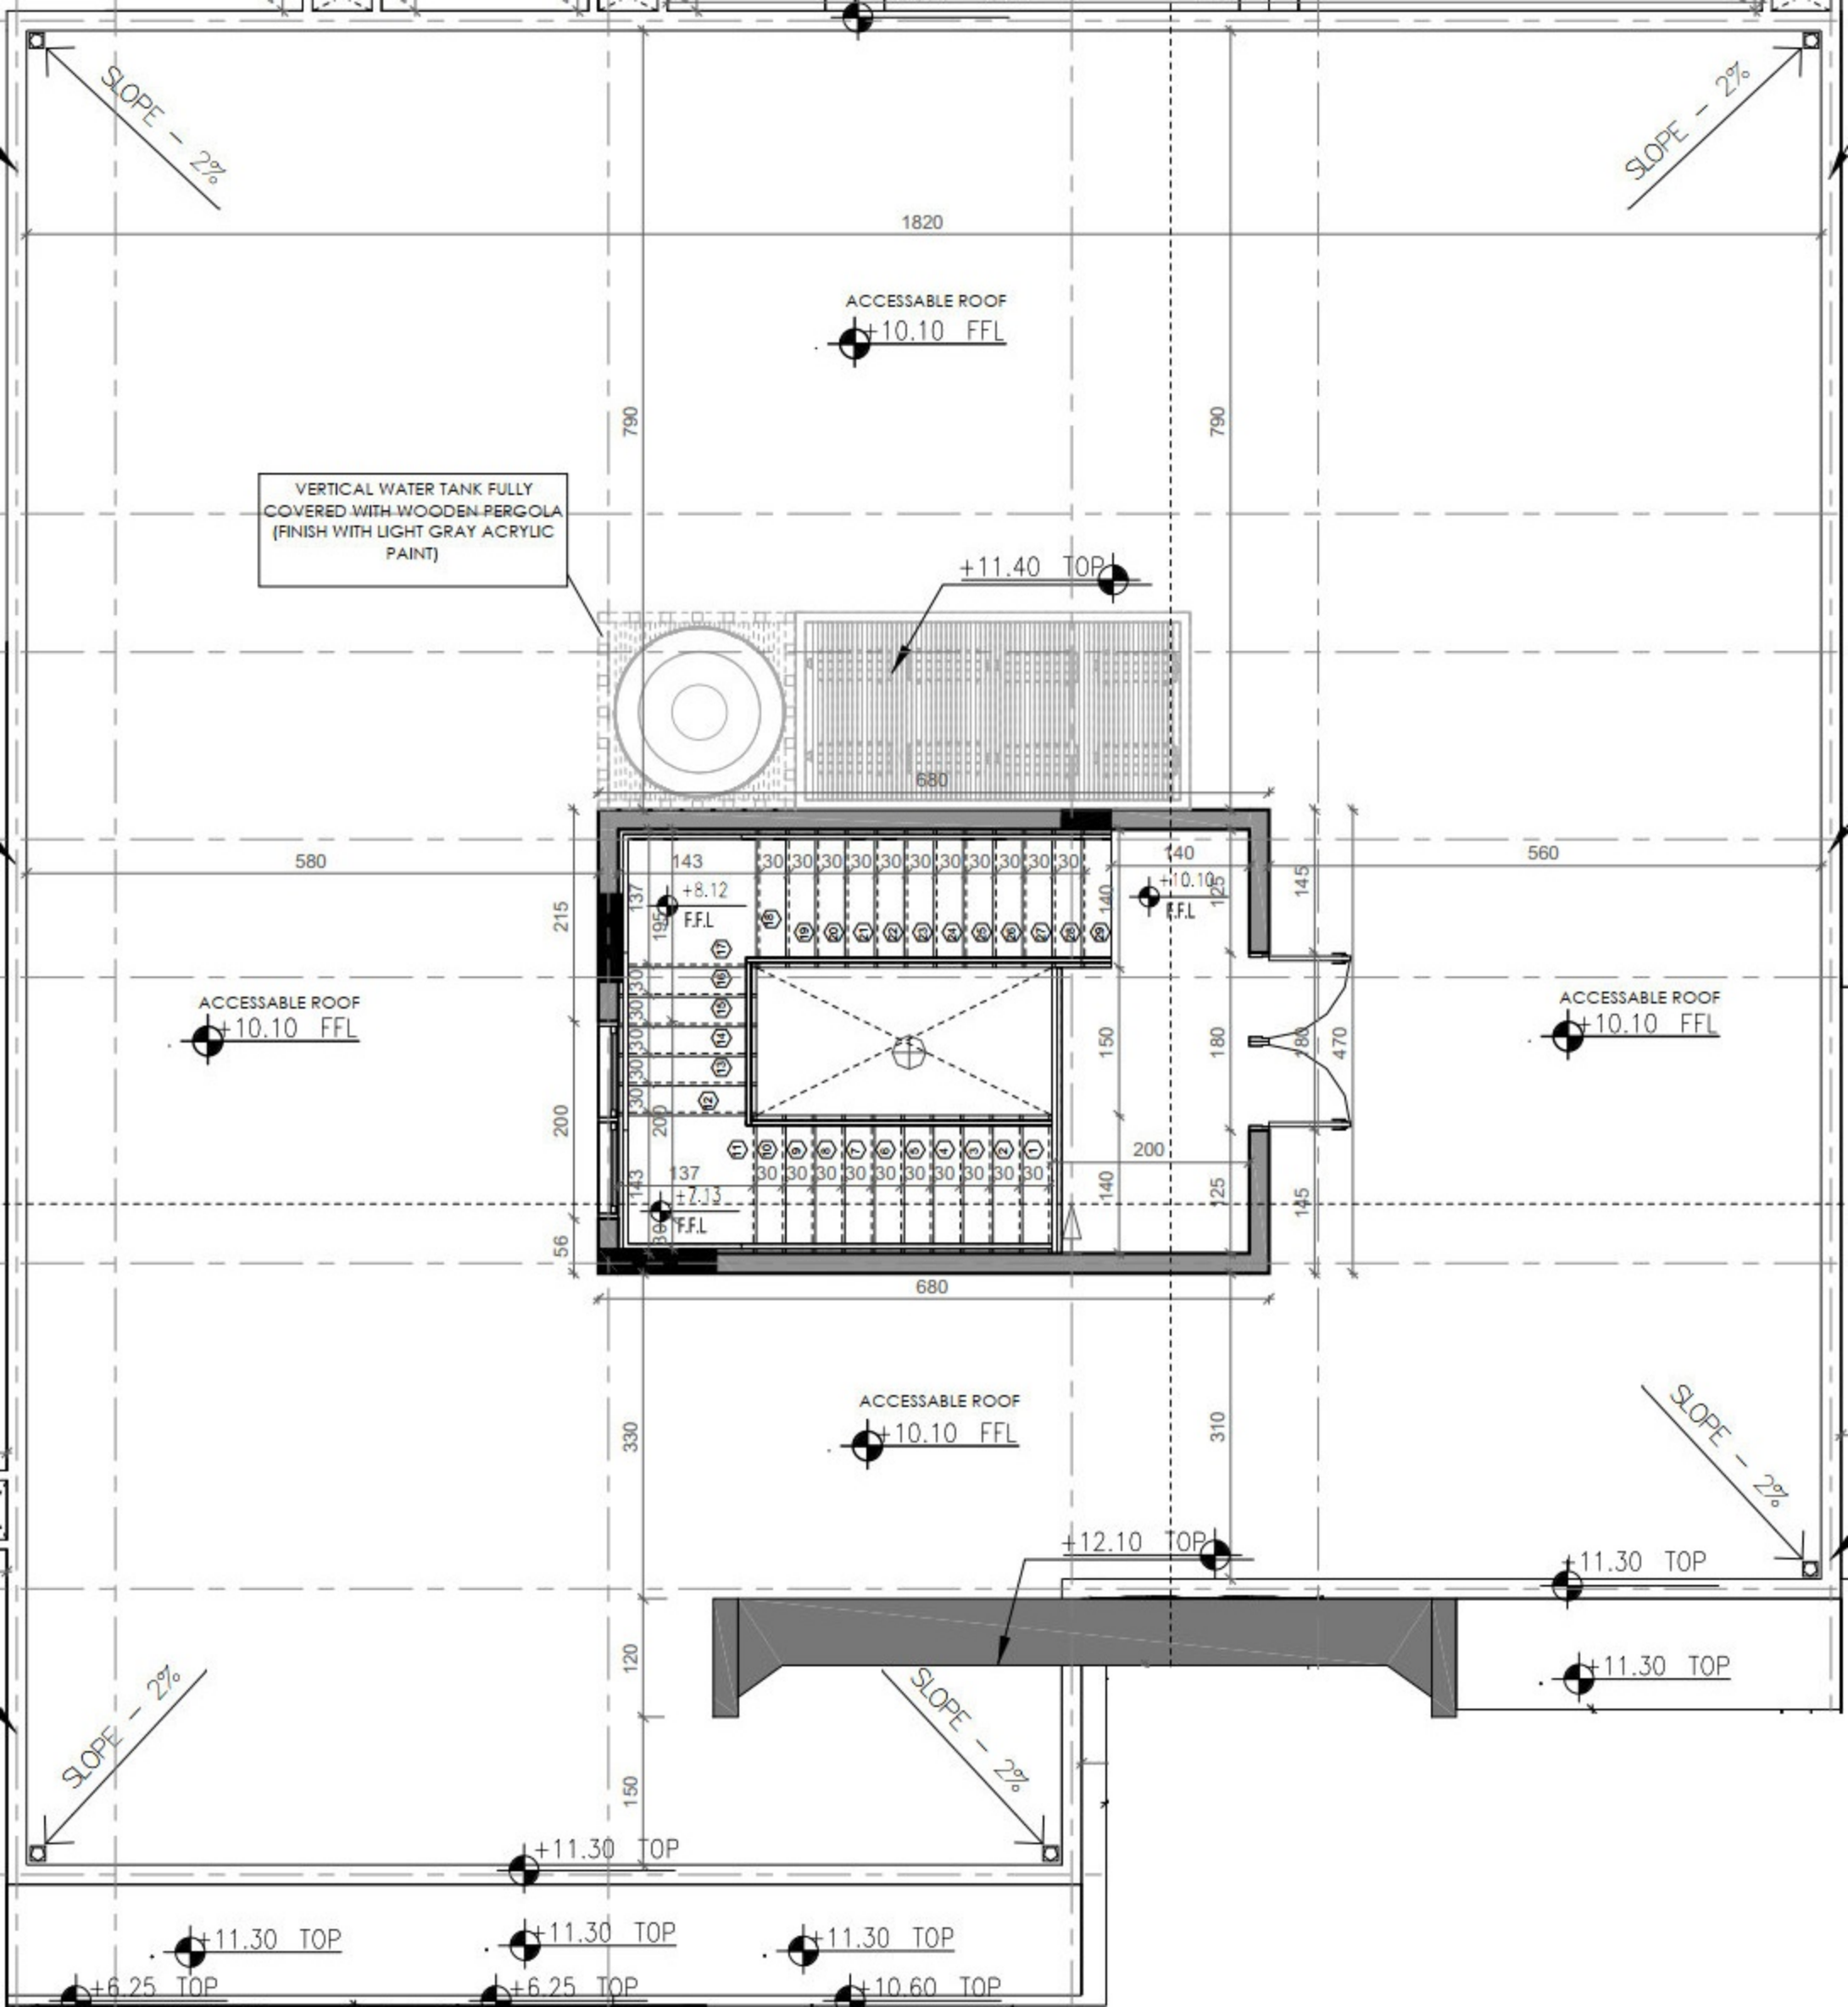
SLOPE – 2%
SLOPE – 2%
1820
ACCESSABLE ROOF
+10.10 FFL
790
790
VERTICAL WATER TANK FULLY COVERED WITH WOODEN PERGOLA (FINISH WITH LIGHT GRAY ACRYLIC PAINT)
+11.40 TOP
680
580
560
143
+8.12
F.F.L
+10.10
F.F.L
215
200
56
680
ACCESSABLE ROOF
+10.10 FFL
ACCESSABLE ROOF
+10.10 FFL
137
+7.13
F.F.L
ACCESSABLE ROOF
+10.10 FFL
330
310
SLOPE – 2%
+12.10 TOP
+11.30 TOP
+11.30 TOP
120
150
SLOPE – 2%
SLOPE – 2%
+11.30 TOP
+11.30 TOP
+11.30 TOP
+11.30 TOP
+6.25 TOP
+6.25 TOP
+10.60 TOP